

STATO DI PROGETTO


Planimetria - quote in cm, superfici in mq



Note
Ridisegno vettoriale della tavola 'Stato di progetto': geometria ricalcata dalle quote in tavola, senza modifiche.

CAMERA 15,956 mq - ARREDO

Disegno dell'arredatore ruotato di 180 gradi e riportato in orientamento di pianta

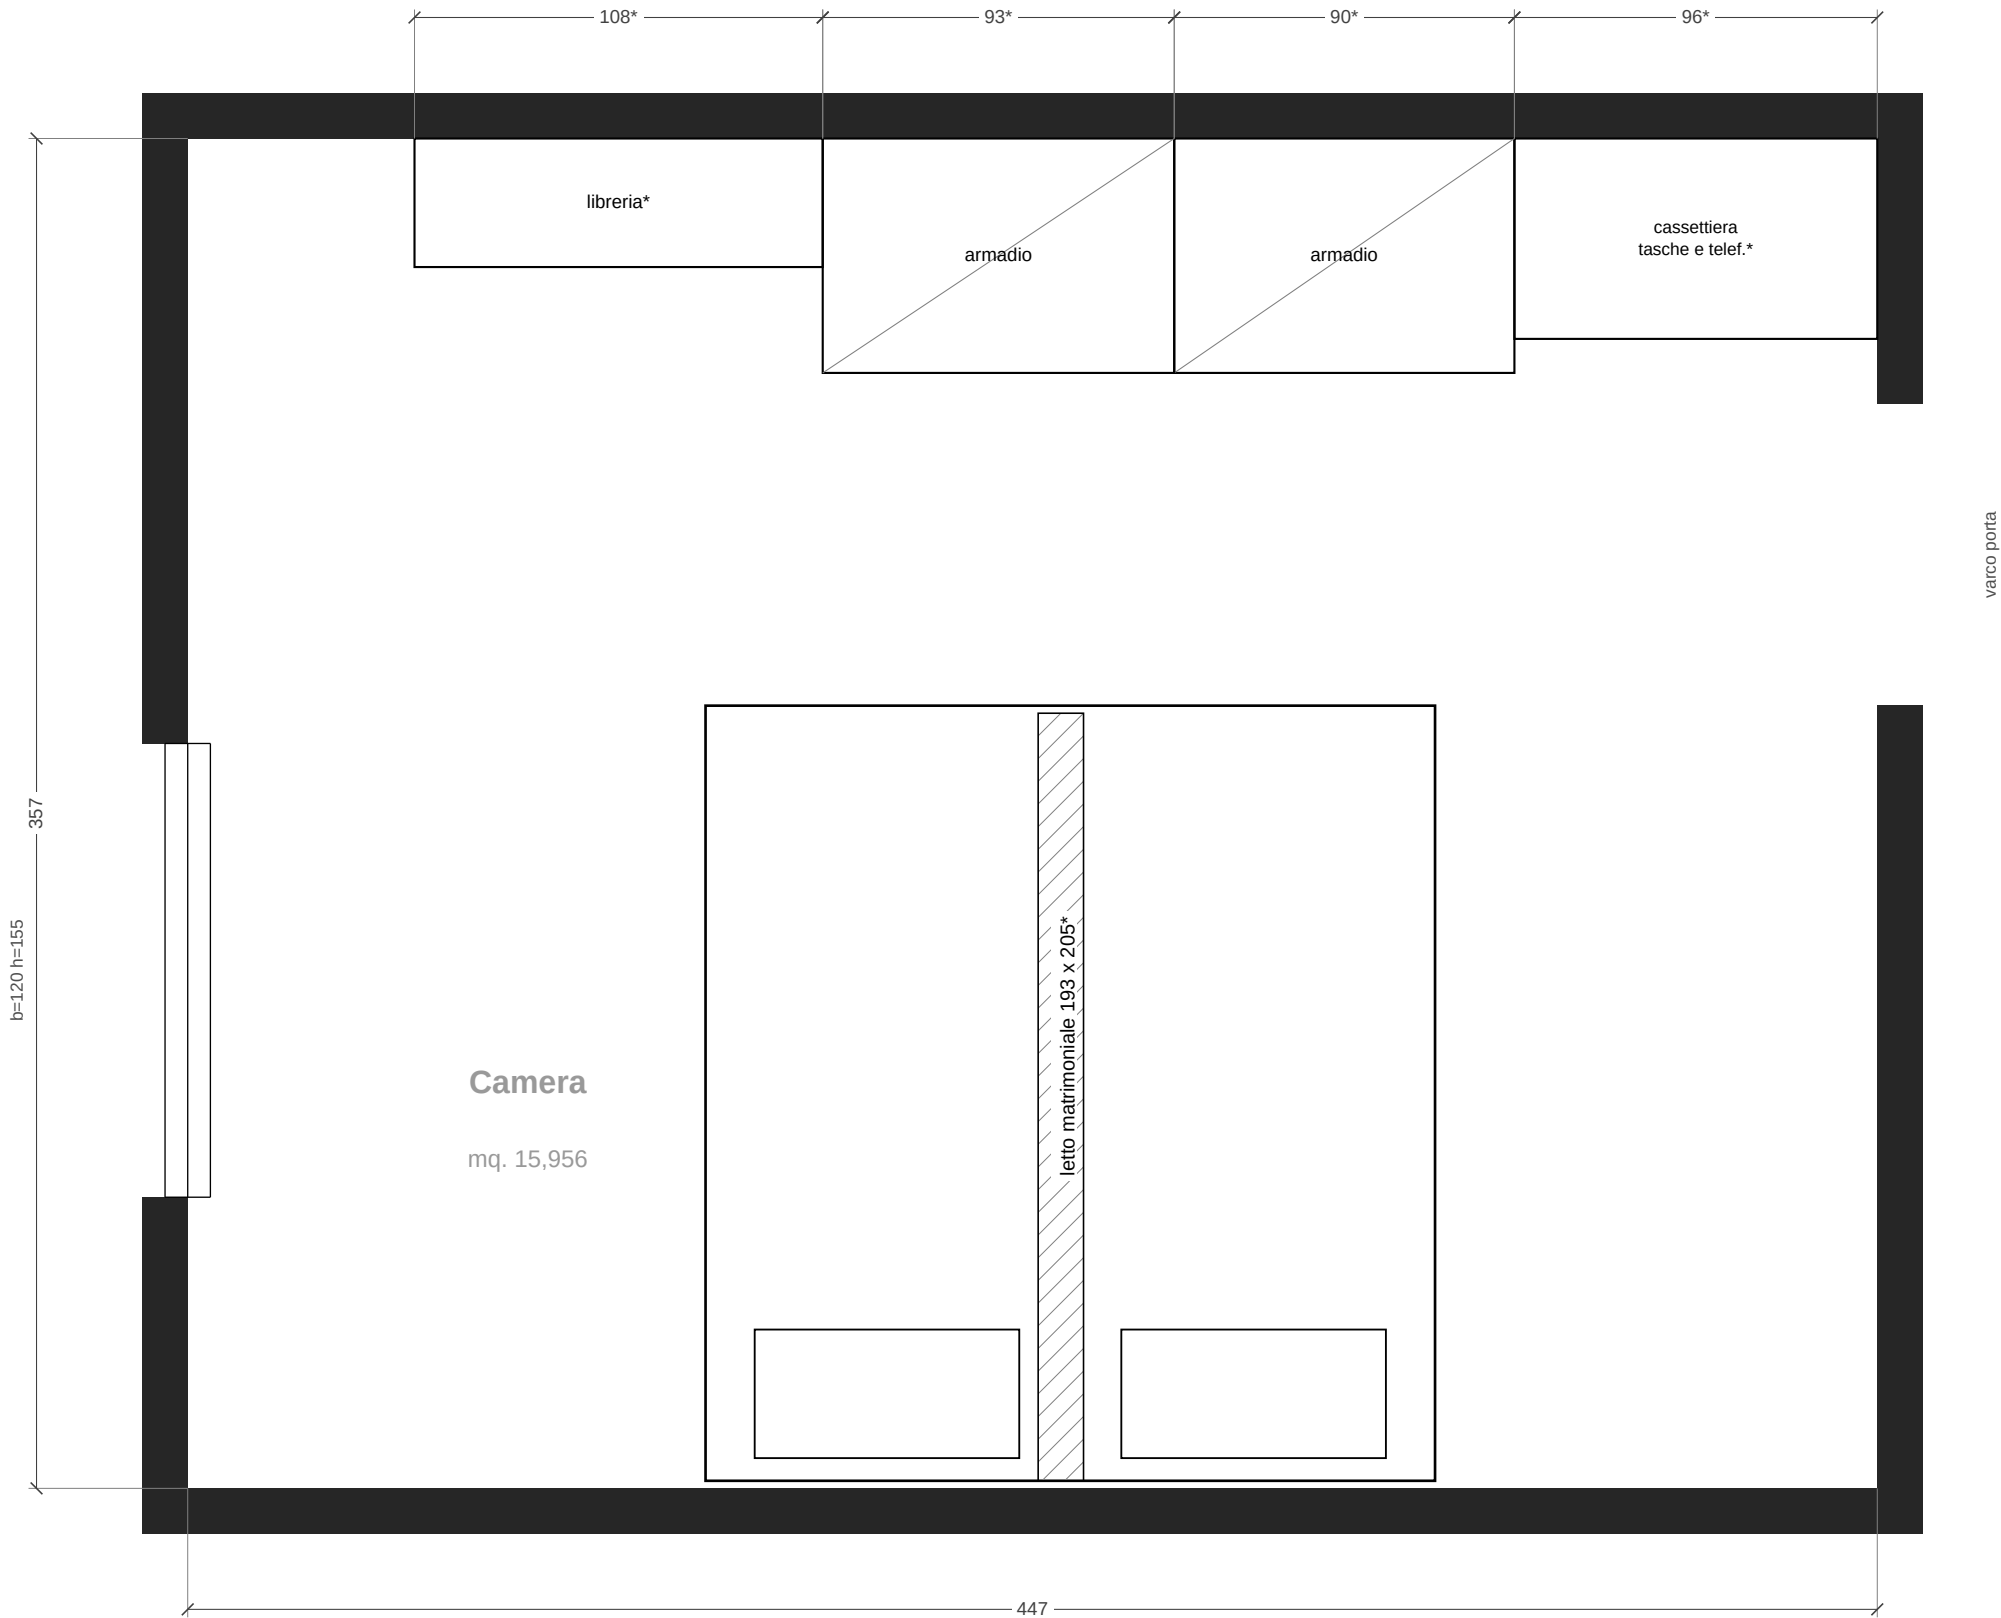

Elementi da verificare (*)

- Testo a mano sulla cassettiera in alto a destra: letto come 'cassettiera, tasche e telef.'.
- Larghezze degli armadi e profondita' (62 / 34 cm) ricavate dallo schizzo a mano, non quotate.
- La striscia tratteggiata al centro del letto (12 cm) e' interpretata come giunzione tra due letti/testiera.
- Restano da chiarire alcune linee sottili a sinistra della parete armadi (forse comodini): non riportate.

APPARTAMENTO - PROGETTO ARREDI


Disegni ripuliti dagli schizzi dell'arredatore e dallo stato di progetto
Ridisegno da immagini: misure non quotate sono ricavate dallo schizzo (verificare in cantiere)

Scala 1:20

Tavola 2 / 9 - 29/09/2026

CAMERA 18,63 mq - ARREDO


Letto matrimoniale, cabina armadio, specchio verso il corridoio

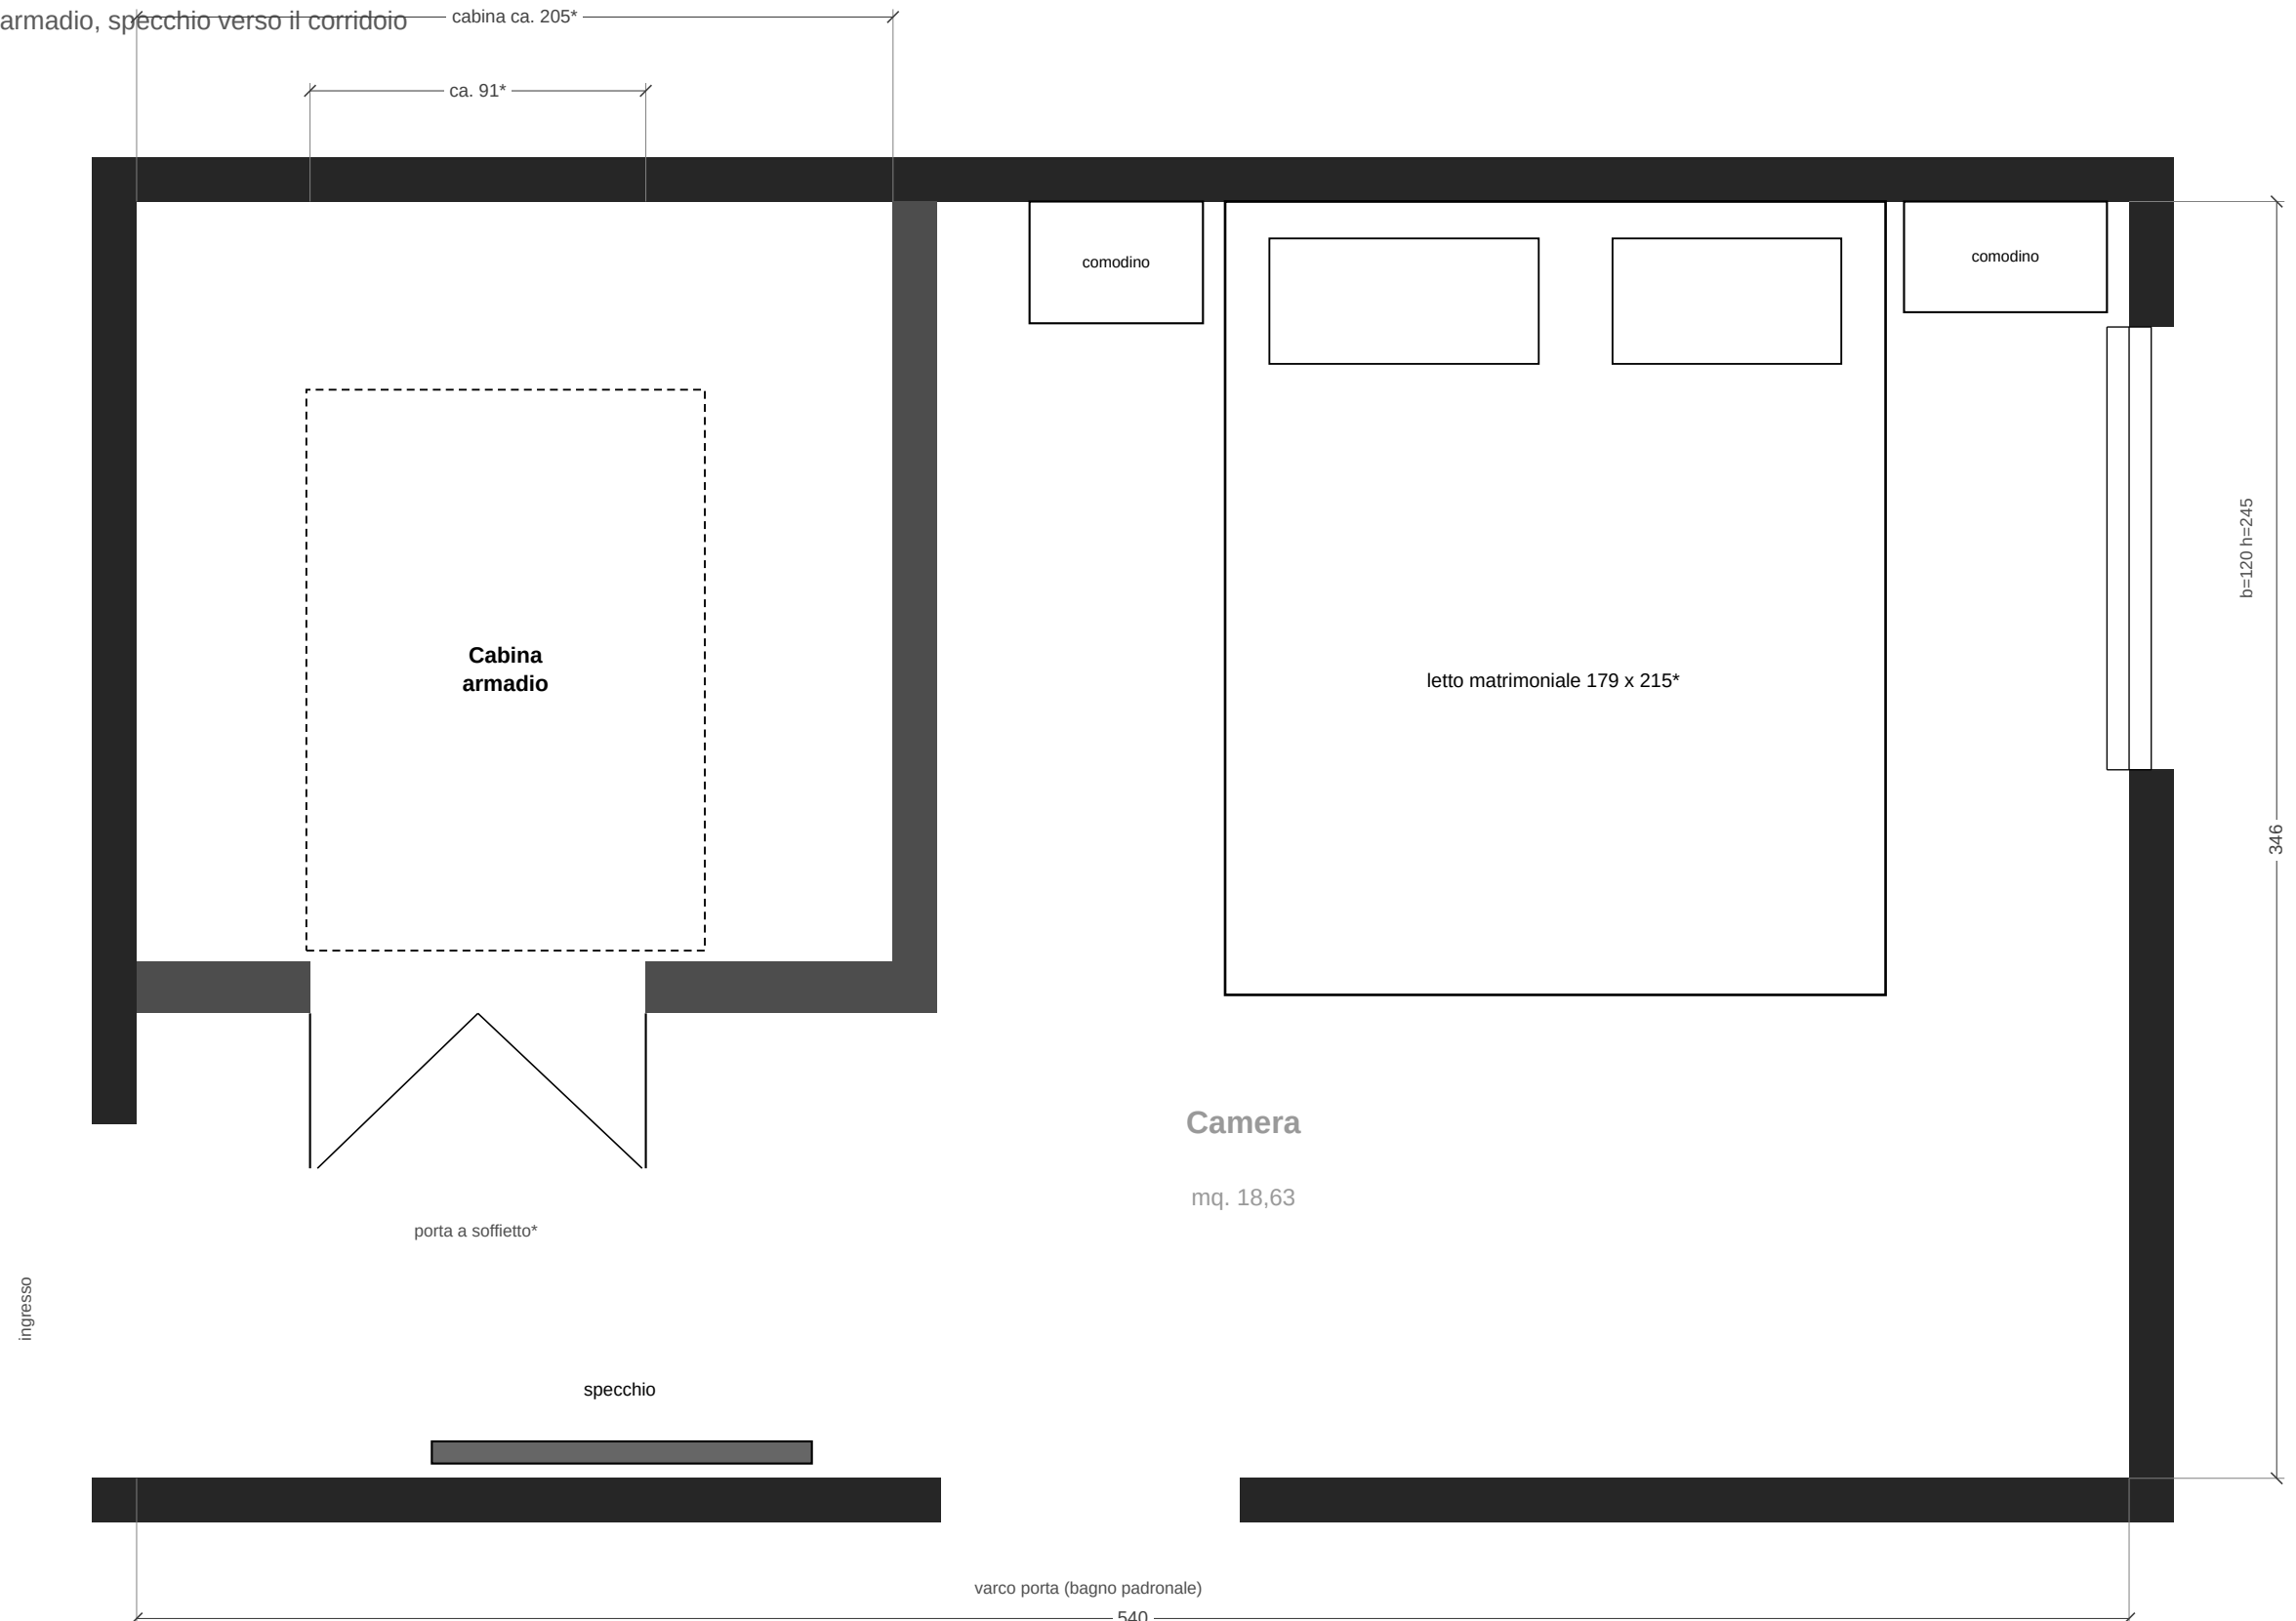**Elementi da verificare (*)**

- Cabina armadio: spessore/posizione delle tramezze e dimensione del mobile interno ricavate dallo schizzo (non quotate).
- Il dettaglio interno della cabina (mensole, cassetti, specchio) e' nella tavola 9 dell'arredatore: non leggibile, non riportato.
- Dimensioni letto e comodini misurate sul disegno.

BAGNO 7,12 mq - ARREDO

Bagno padronale (accessibile dalla camera 18,63)

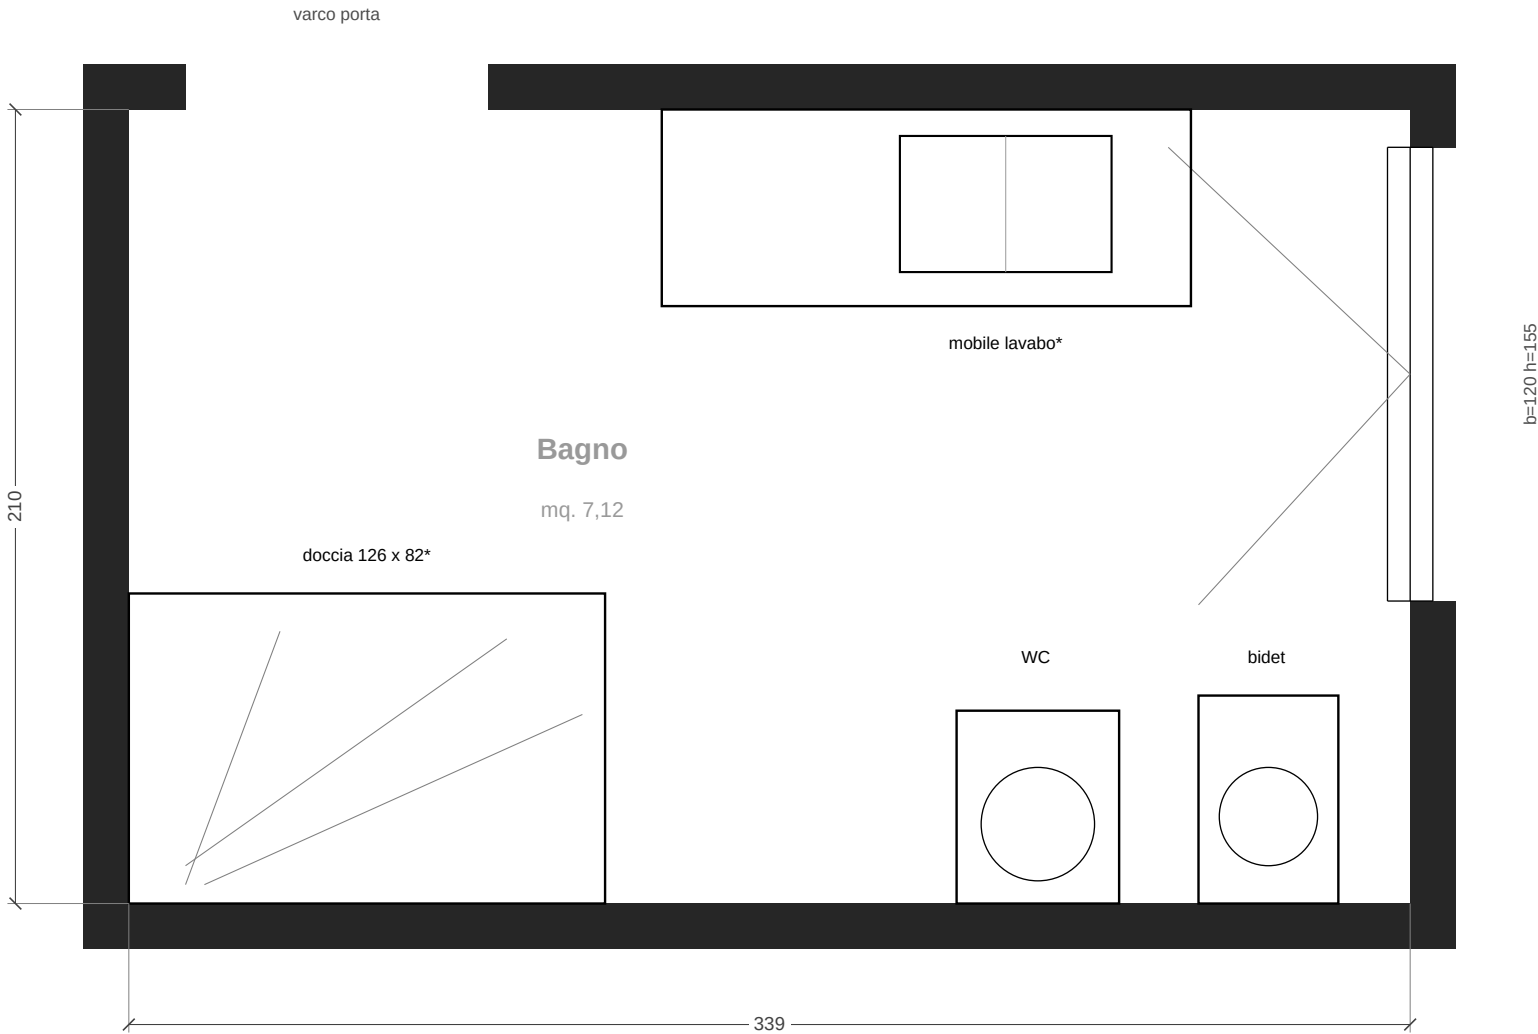


Elementi da verificare (*)

- Doccia, mobile lavabo e sanitari misurati sullo schizzo (non quotati).
- Le linee oblique accanto alla finestra sono l'apertura dell'anta, non un arredo.

BAGNO 7,22 mq - ARREDO

Bagno con lavatrice/asciugatrice in nicchia

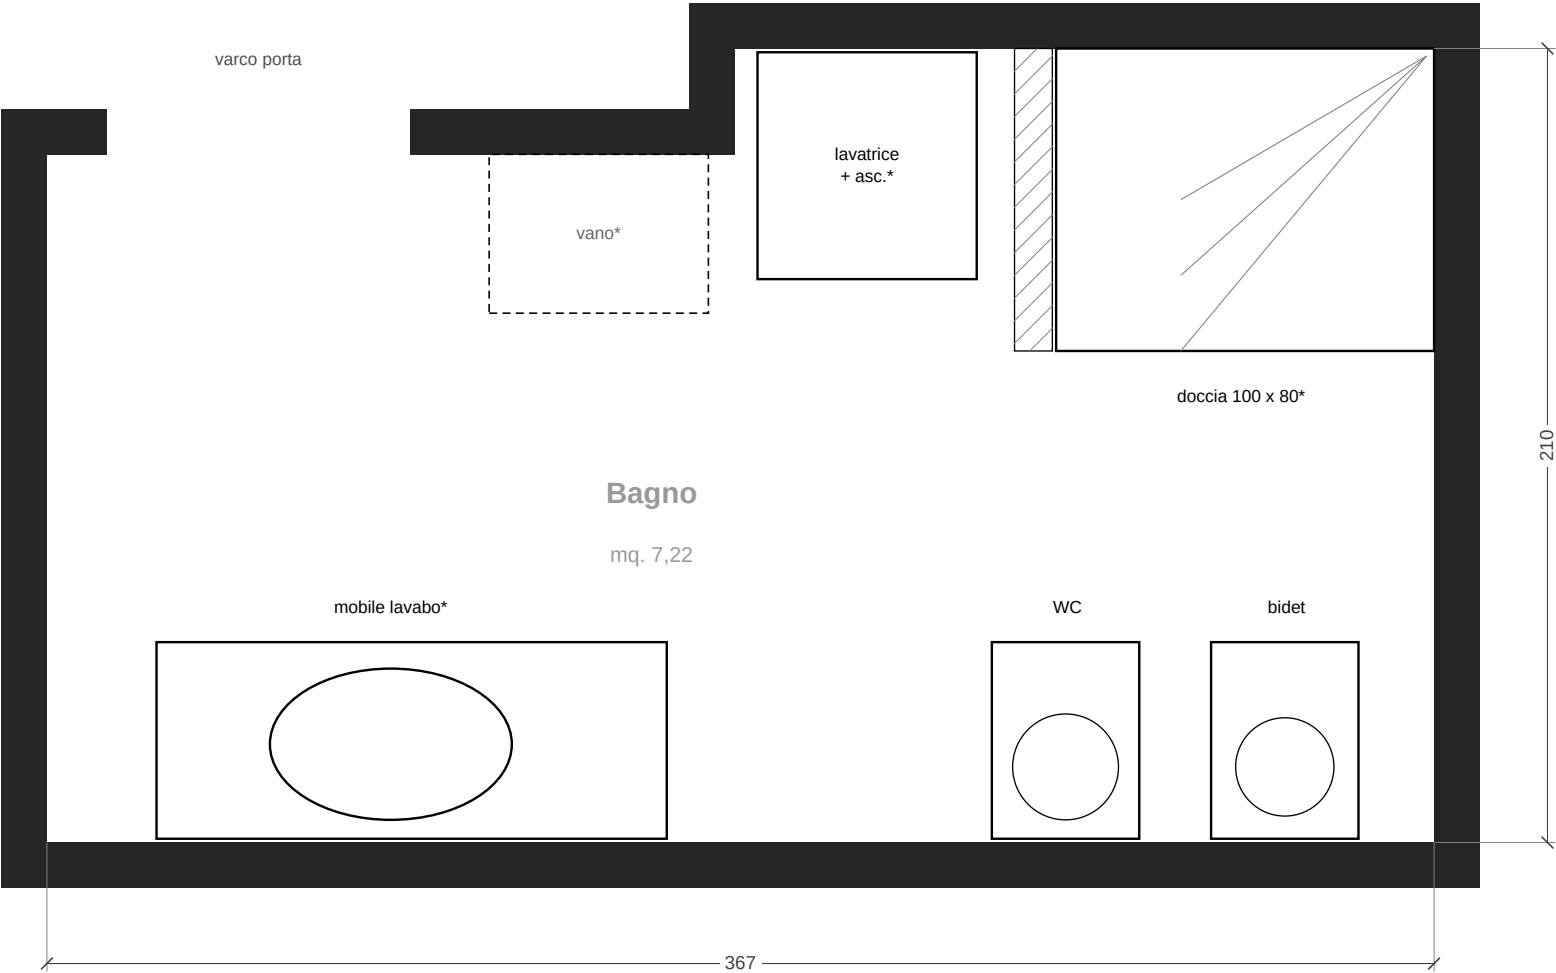


Elementi da verificare (*)

- La scritta sulla nicchia in alto e' letta come 'lavatrice / asc.' (asciugatrice), scritta capovolta nello schizzo.
- Il vano a sinistra della lavatrice (linea diagonale) non e' etichettato: riportato tratteggiato.
- Dimensioni di doccia e sanitari misurate sullo schizzo.

CUCINA - VERSIONE 1

Schizzo dell'arredatore ripulito - lato lungo con lavello e piano cottura, ritorno sotto la finestra

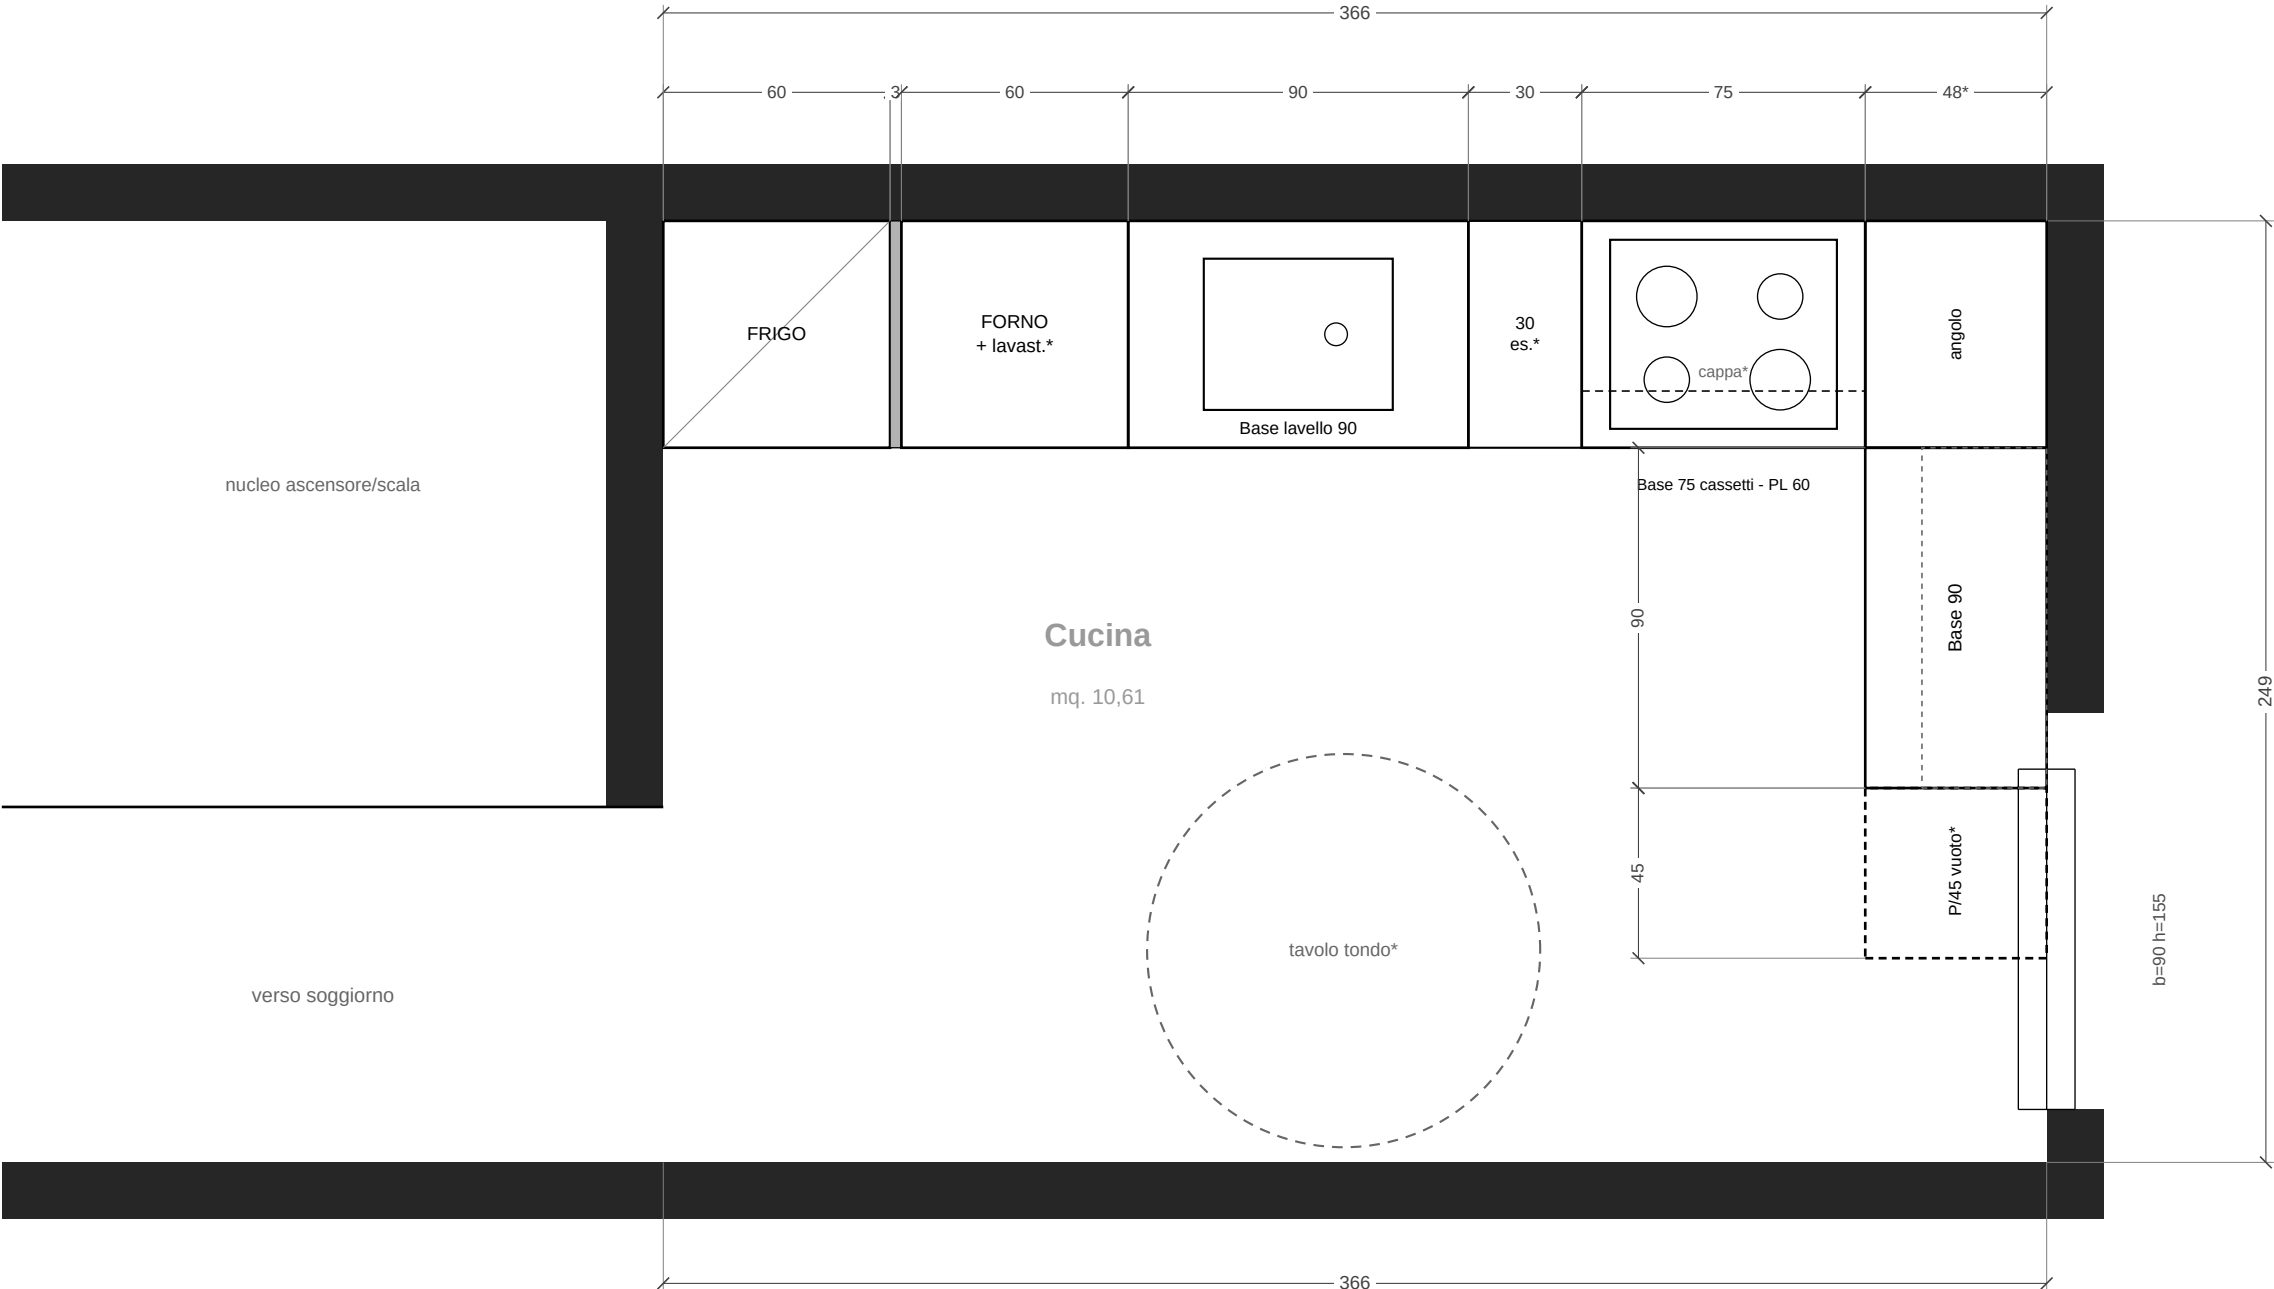


Elementi da verificare (*)

- 'Forno + lavas.' letto come forno in colorina con lavastoviglie/cassetto; '30 es.' come modulo da 30 (estraibile?); 'P/45 vuoto x Tv' come vano da 45 (da chiarire).
- Profondita' del ritorno (48 cm) ricavata per differenza: $366 - (60+3+60+90+30+75) = 48$. Profondita' fila principale 60 cm come standard.
- Cappa, mensole (tratteggiate sul ritorno) e tavolo tondo (circa 105 cm) sono indicativi, cosi' come tracciati a mano.
- Il render 3D allegato (Arredo3, 29/09/2026) corrisponde a questa versione: lavello e piano cottura sulla parete lunga, ritorno sotto la finestra.

CUCINA - VERSIONE 2

Schizzo dell'arredatore ripulito - lavello sul lato finestra, piano cottura sulla parete lunga

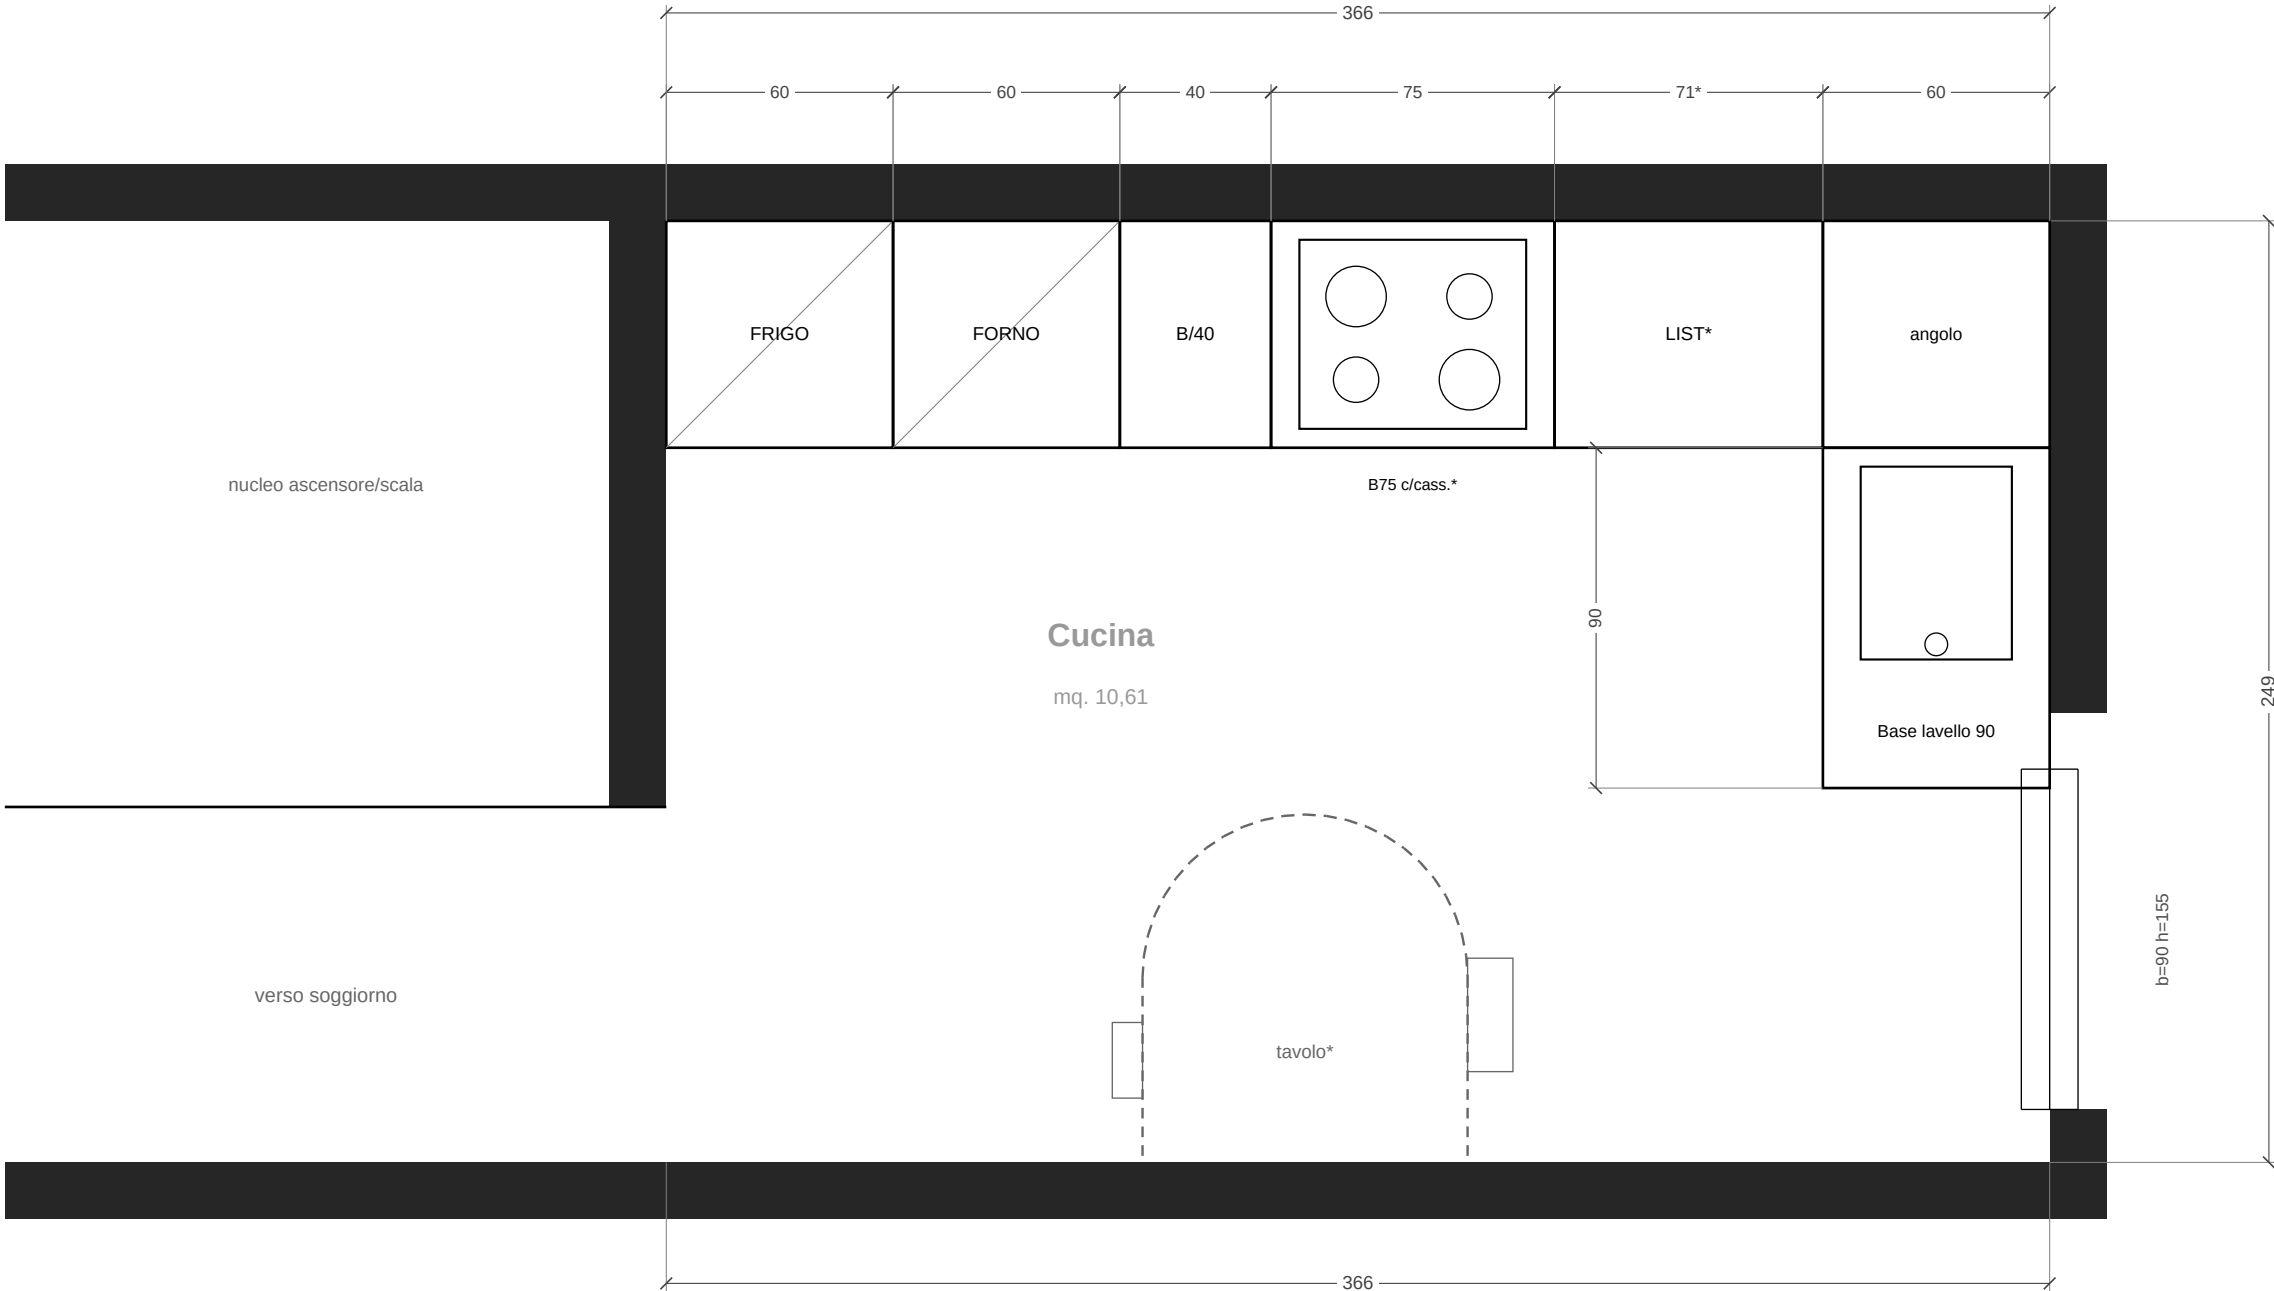


Elementi da verificare (*)

- 'B75 c/cas' letto come base da 75 con cassetti + piano cottura (le due croci); 'LIST' non chiaro (listello / modulo di chiusura): 71 cm ricavati per differenza.
- Angolo e ritorno lato finestra (profondita' 60) ricavati dallo schizzo; la 'Base Lav.' del ritorno e' letta come base lavello da 90 con lavello.
- Tavolo: nello schizzo e' un arco con due sedute; qui e' reso come tavolo con lato curvo (forma da confermare).

ZONA GIORNO - ARREDO

Soggiorno/pranzo e cucina: posizioni indicative dal disegno dell'arredatore (ruotato di 90 gradi)

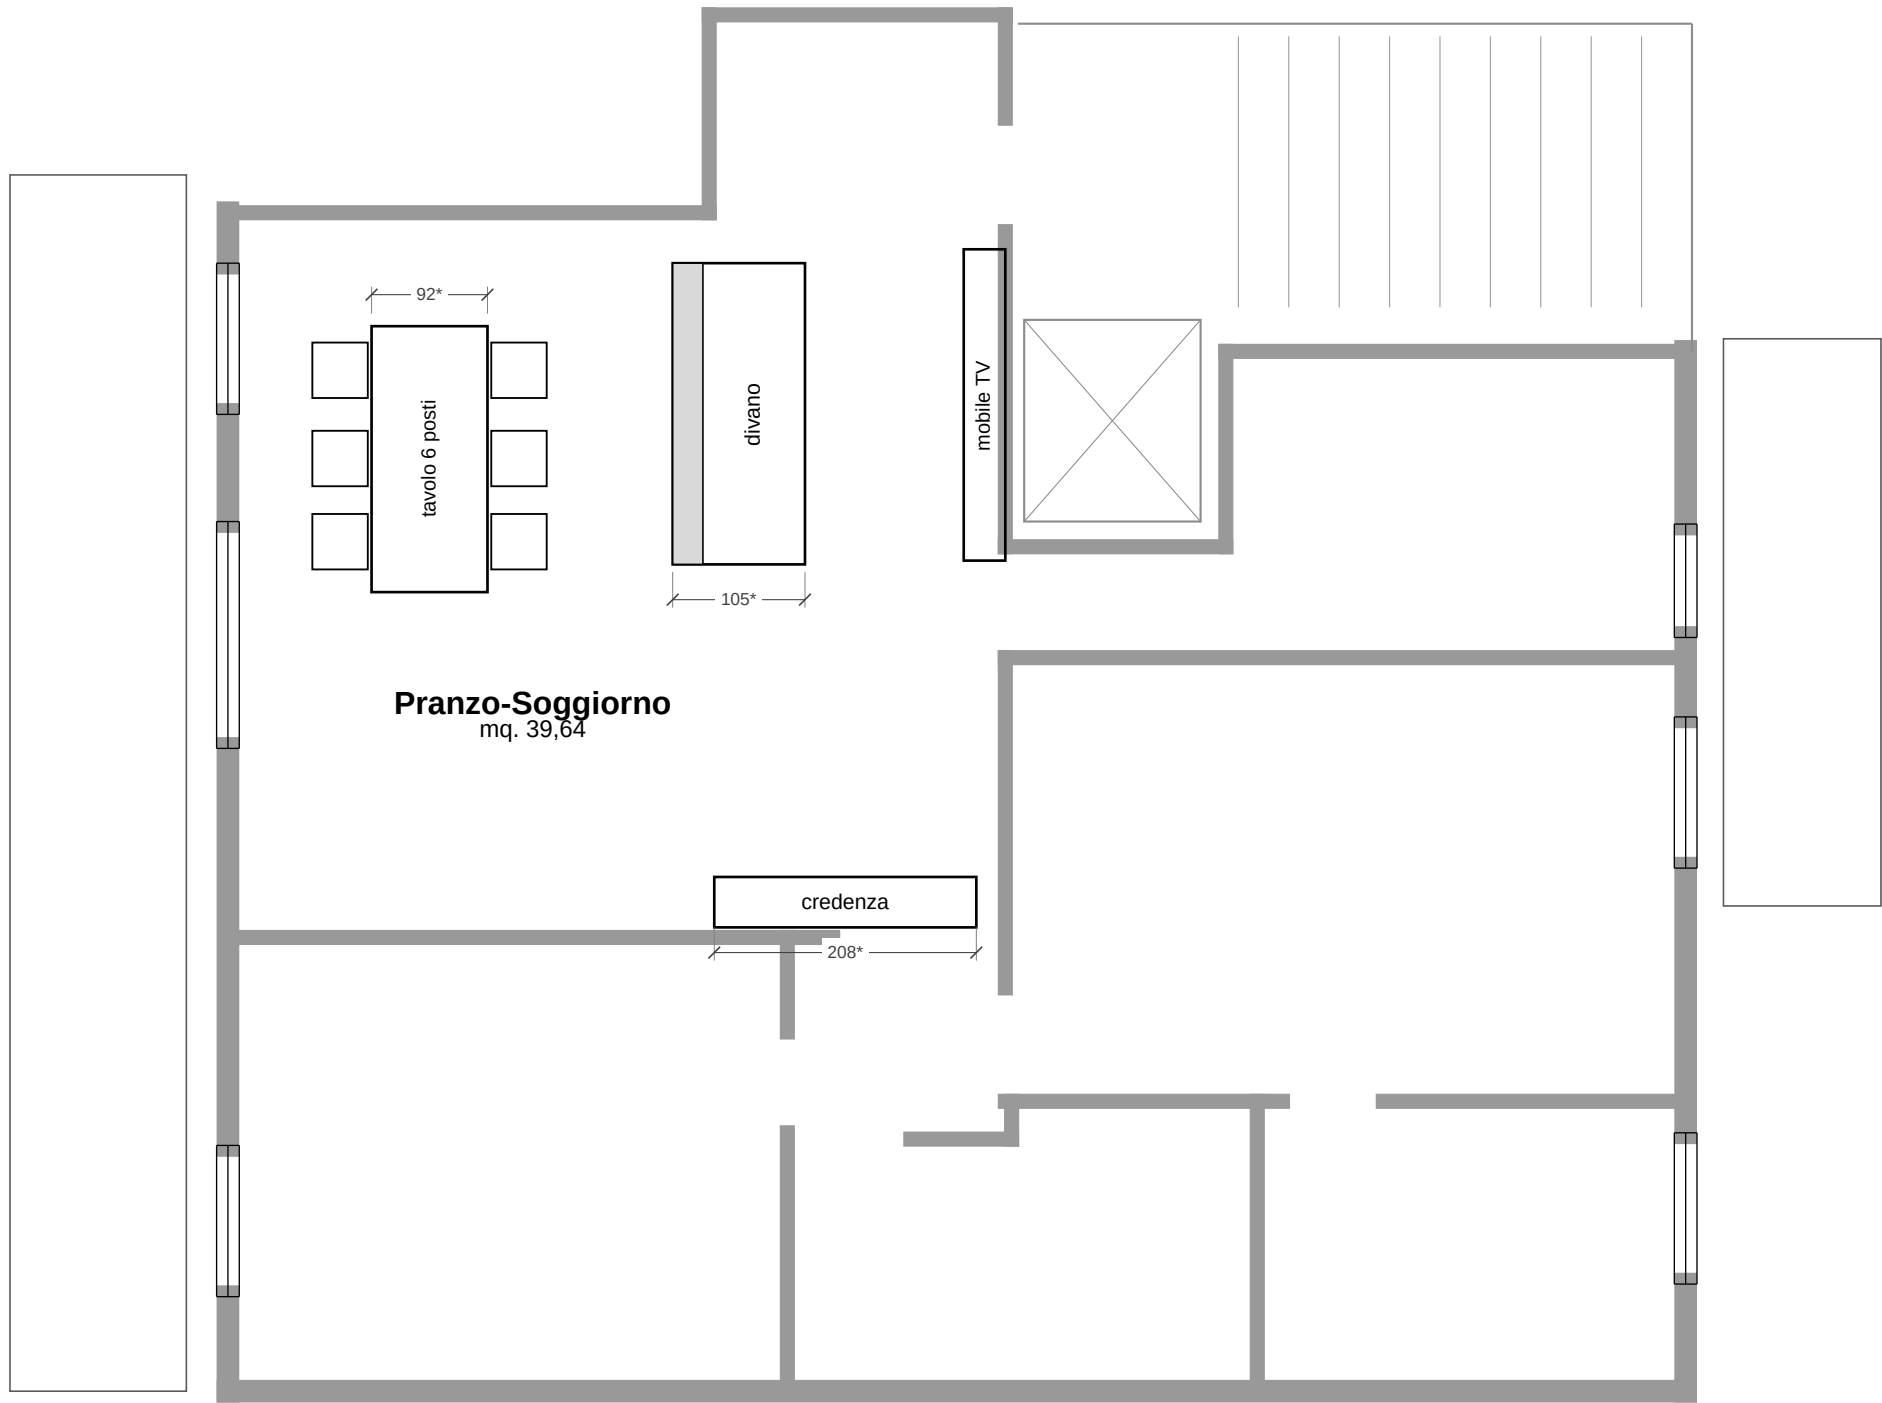

Elementi da verificare (*)

- Lo schizzo dell'arredatore e' ruotato di 90 gradi e senza quote: le posizioni sono ricavate per allineamento con le pareti (TV sul nucleo scala, credenza sulla parete verso le camere).
- Misure di tavolo, divano, mobile TV e credenza da confermare sul disegno originale/in cantiere.
- Il dettaglio a sinistra-in-basso dello schizzo (mensole, ganci, cassetti, specchio) appartiene alla cabina armadio della camera 18,63: non leggibile, non riportato.

NOTE E PUNTI DA VERIFICARE

Riepilogo delle letture incerte degli schizzi a mano

Cucina versione 1

- 'Forno + lavas.': forno in colonna con lavastoviglie o cassetto sotto?
- '30 es.': modulo da 30 cm - estraibile / espositore?
- 'P/45 vuoto x Tv': vano da 45 cm - a cosa e' destinato?
- Profondita' del ritorno lato finestra: 48 cm (per differenza) o 45?
- Cappa e mensole sul ritorno: solo indicate a mano.

Cucina versione 2

- 'B75 c/cas': base 75 con cassette + piano cottura? 'LIST' cos'e' esattamente (71 cm per differenza)?
- Base lavello sul ritorno (90 cm) con profondita' 60: verificare col fornitore.
- Forma del tavolo (arco con due sedute nello schizzo).

Camere

- Camera 15,956: scritta 'tasche e telef.' e larghezza armadi; striscia centrale sul letto.
- Camera 18,63: cabina armadio - tramezze, mobile interno, porta a soffietto e dettaglio interno (tavola 9).

Bagni

- Bagno 7,12: finestra b/h non compilate nello schizzo (uso i valori dello stato di progetto: b=120 h=155).
- Bagno 7,22: 'lavatrice + asc.' letta da scritta capovolta; vano a sinistra non etichettato.

Generale

- Tutte le quote non scritte sono ricavate misurando gli schizzi: verificare in cantiere prima degli ordini.
- Il render 3D (Arredo3) non e' stato ridisegnato: corrisponde alla versione 1.